

IMPLANTATION PHOTOVOLTAÏQUE — BÂTIMENT C : TERRASSE ÉCOLE SUPTECH

Relevé contradictoire du 27/07/2026 — terrasse complète 26,2 × 51,1 m (plan) — bleu = mesuré · orange = à confirmer · gris = déduit — cage 4,11×≈8,82 (arrondi annoncé ≈8,5) · local 4,18×4,50 à 7,92 · ouvrage bas 4,78×≈1,0 — aucune souche, aucun équipement de climatisation au relevé — tables E-O portrait 1,134×4,70 (15°), allées de maintenance 1,90 (compte identique à 0,60 — démontré)


Capacité démontrée sur le relevé : 314 modules — ENGAGÉ AU MARCHÉ : 288 modules (marge +26)

Implantation définitive arrêtée après relevé d'exécution — marché à prix unitaires

terrasse complète 51,1 m (allées de maintenance 1,90 / rives 0,35 / dégagt 0,30 (ouvrage bas 0,50)) : 314 mod. = 196,25 kWc — variante conservatrice 1,50/0,50/0,50 : 314 — engagement 288 mod. = 180,0 kWc

cage : segment cage→local RELEVÉ 7,92 → profondeur ≈8,82 déduite de la fermeture 51,1 (valeur arrondie annoncée au relevé : ≈8,5) — à confirmer à l'exécution

Δ 0,58 (plan — mesuré) à confirmer

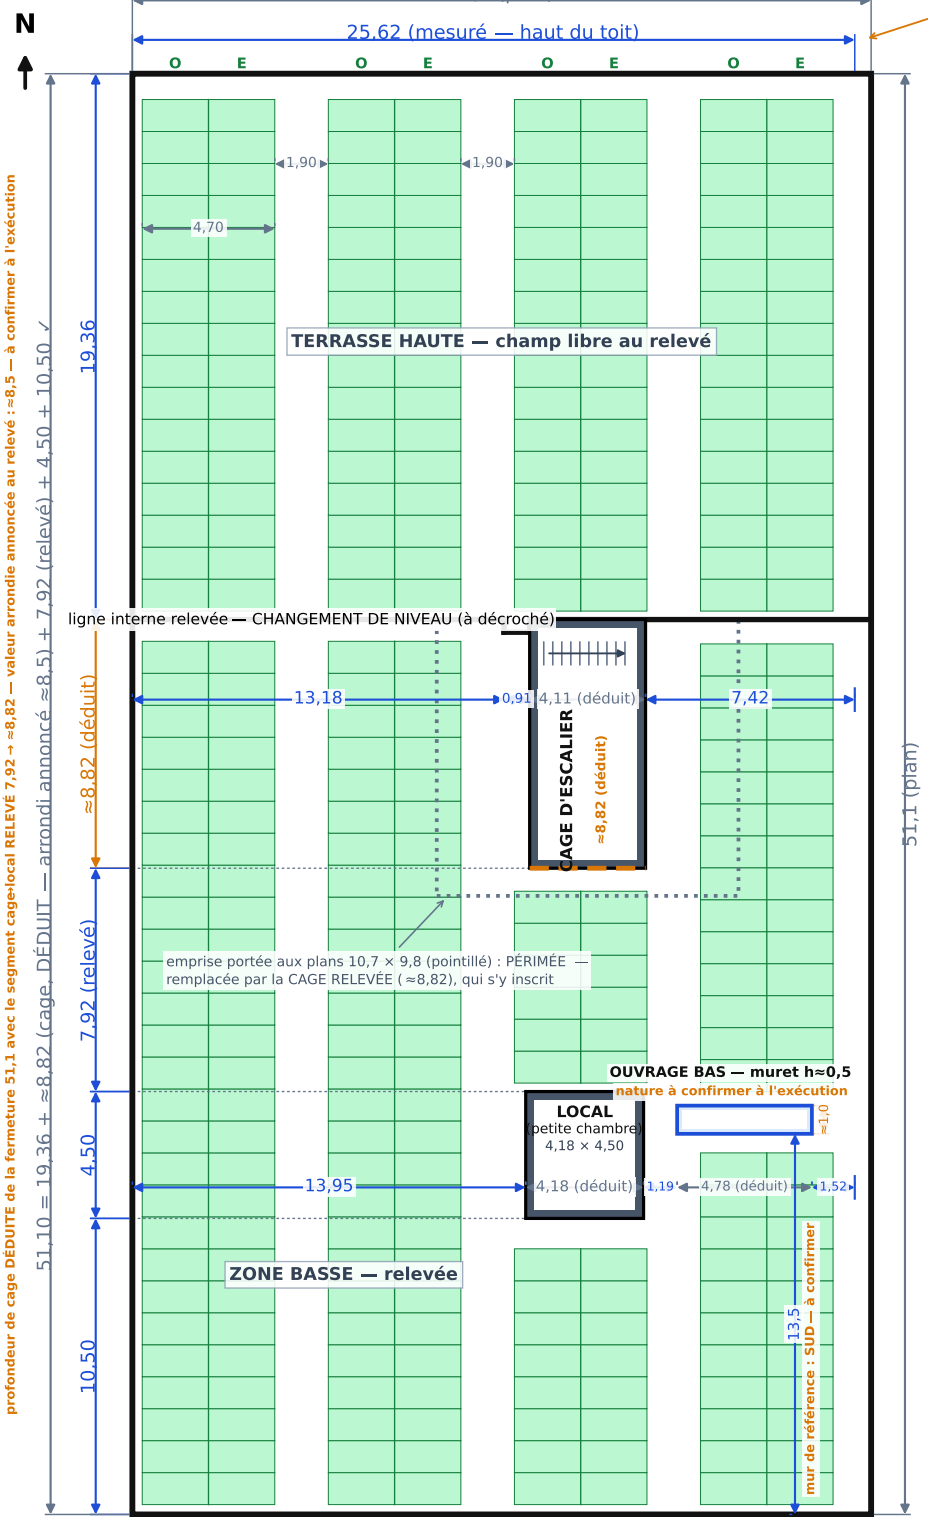

LÉGENDE

- table E-O portrait 1,134×4,70 — 2 modules 625 Wc, pose 15°
- volume relevé (cage 4,11×≈8,82 déduit · local 4,18×4,50)
- ouvrage bas 4,78×≈1,0 — muret h≈0,5 · dégagement 0,50
- emprise portée aux plans — périmée (cage relevée retenue)
- cote MESURÉE au relevé contradictoire (bleu)
- cote / position À CONFIRMER À L'EXÉCUTION (orange)
- cote de plan / déduite des fermetures (gris)

CONTRÔLES DE FERMETURE DU RELEVÉ


13,18 + 0,91 (marche) + 4,11 (déduit) + 7,42 = 25,62 ✓ exact
13,95 + 4,18 (déduit) + 1,19 + 4,78 (déduit) + 1,52 = 25,62 ✓
19,36 + ≈8,82 (cage, DÉDUIT) + 7,92 (relevé) + 4,50 + 10,50 = 51,10 ✓
→ segment cage→local = 7,92 RELEVÉ le 27/07/2026 ; le seul tronçon déduit est la PROFONDEUR DE LA CAGE (arrondi annoncé au relevé : ≈8,5) — à confirmer à l'exécution
largeur : 25,62 mesuré vs 26,2 plan → Δ 0,58 à confirmer
angle SE : le petit rectangle = l'OUVRAGE BAS (4,78 × ≈1,0) · 1,19 = écart local+ouvrage · 13,5 = ouvrage → mur sud

CALEPINAGE — PORTRAIT 15°

4 rangées de tables E-O PORTRAIT 1,134 × 4,70 (2 × 2,382 × cos15° + faitage) le long des 51,1 m retenu : allées de MAINTENANCE 1,90 m (prescription : 0,60 mini) — le calcul exhaustif donne le même compte pour TOUTE allée de 0,60 à 1,94 m : 1,90 ne coûte AUCUN module → cage+local+marche ne coupent qu'1 bande ; ouvrage bas : 1 rives 0,35 · dégagt 0,30 (ouvrage bas : 0,50) information : uniforme 0,60 = 314 · conservateur 1,50/0,50 = 314 rive est 0,77 + allées : une 5e rangée exigerait 26,60 m de largeur (5×4,70 + 4×0,60 + 2×0,35) > 25,62 disponibles coupure de niveau à la ligne interne (aucun chevauchement) CAPACITÉ DÉMONTREE sur 51,1 m : 314 mod. = 196,25 kWc ENGAGÉ AU MARCHÉ : 288 modules (18×16) = 180,0 kWc 18 strings × 16 — 3 onduleurs 50 kW (96/96/96) marge de capacité : +26 modules

À CONFIRMER À L'EXÉCUTION (orange)

profondeur de la cage ≈8,82, déduite de la fermeture 51,1 (valeur arrondie annoncée au relevé : ≈8,5)
ouvrage bas de l'angle SE : profondeur ≈1,0 · muret h≈0,5 · nature de l'ouvrage · mur de référence de la cote 13,5 (sud)
Δ de largeur 0,58 entre plan (26,2) et relevé (25,62)
implantation des équipements de climatisation à venir — aucun sur la terrasse au relevé, à coordonner avec le champ PV

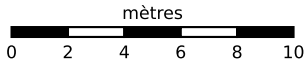

Relevé contradictoire du 27/07/2026 : terrasse COMPLÈTE (bord bas = mur sud) — un seul calepinage sur 51,1 m. Aucune table à cheval sur la ligne interne.
OUVRAGE BAS (angle SE) : 4,78 × ≈1,0 — muret h≈0,5, nature à confirmer à l'exécution — dégagement 0,50 · aucune souche relevée sur la terrasse.
Aucun équipement de climatisation présent sur la terrasse au relevé ; une installation ultérieure sera coordonnée avec le champ PV à l'exécution.

ACCORDIA TECH — Consultation FRDISI : PV + stockage, Mohammedia

BÂT. C — TERRASSE ÉCOLE SUPTECH — IMPLANTATION PHOTOVOLTAÏQUE

Document 05H_IMPLANTATION_BAT_C_ECOLE — Statut : Appel d'offres

Date : Juillet 2026 — Indice : H — relevé contradictoire du 27/07/2026

Échelle : barre graphique (impression A3) — cotes en mètres