


VUE DE TOITURE — BÂTIMENT A (AILE EN L) — RÉSIDENCE UNIVERSITAIRE UIB, MOHAMMEDIA — V2

Contour, locaux et obstacles : RELEVÉ CONTRADICTOIRE du 27/07/2026 (croquis A/B/C) — INTÈGRE LES DÉCISIONS CLIENT DU 27/07 : grand rectangle de la jonction = NÉANT · angle sud-est de l'aile = ANGLE DROIT · TABLES MIXTES autorisées partout
calepinage V2 : tables E-O MIXTES portrait 1,134×4,70 et paysage 2,382×2,25 (2 modules 625 Wc, 15°), FAÏTAGE NORD-SUD (modules face E et face O), rangées N-S continues sur tout le L, positions EXPLICITES
allées 0,60 mini OPTIMISÉES, rives 0,35, dégagement 0,30 (0,50 nature inconnue) — BLEU = mesuré · ORANGE = à confirmer · GRIS = plan/déduit

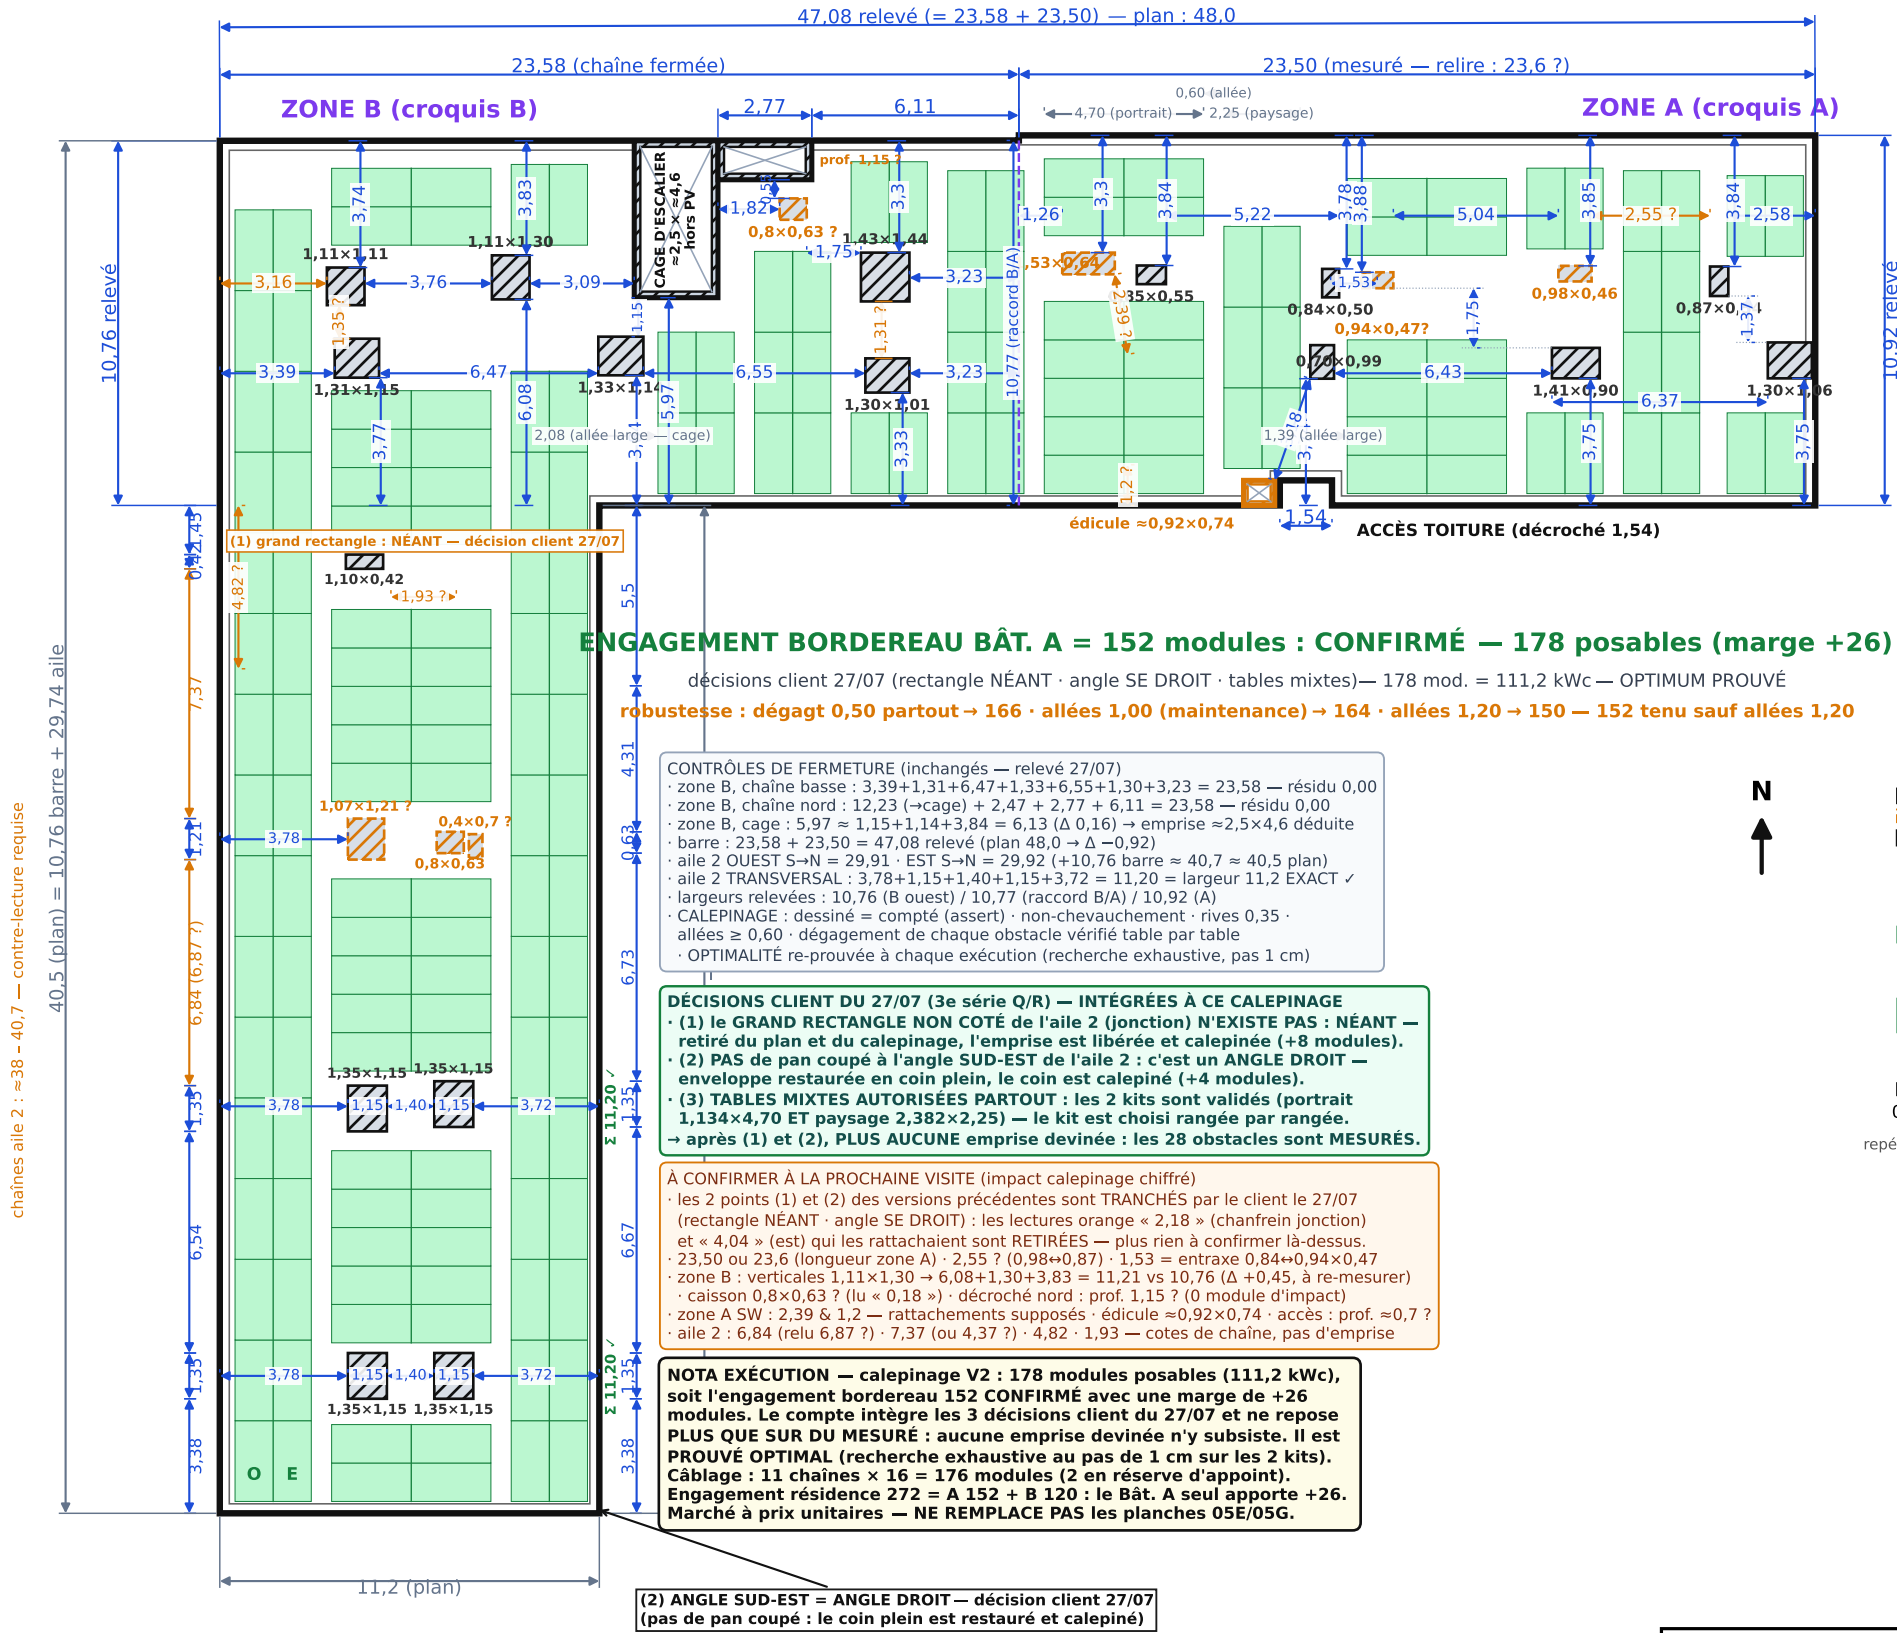

CALEPINAGE V2 — RANGÉES EXPLICITES (kits mixtes)

rg	kit	emprise E-O	portée	mod.
1	PAYSAGE	0,45+ 2,70	L complet	32
2	PORTRAIT	3,30+ 8,00	L complet	46
3	PAYSAGE	8,60+10,85	L complet	30
4	PAYSAGE	12,93+15,18	barre	4
5	PAYSAGE	15,78+18,03	barre	6
6	PAYSAGE	18,63+20,88	barre	4
7	PAYSAGE	21,48+23,73	barre	8
8	PORTRAIT	24,33+29,03	barre	14
9	PAYSAGE	29,63+31,88	barre	6
10	PORTRAIT	33,27+37,97	barre	12
11	PAYSAGE	38,57+40,82	barre	4
12	PAYSAGE	41,42+43,67	barre	8
13	PAYSAGE	44,48+46,73	barre	4

TOTAL DESSINÉ = COMPTÉ : 178 mod. = 111,2 kWc
OPTIMUM PROUVÉ (exhaustif, pas 1 cm)
engagement bordereau 152 → CONFIRMÉ (+26)


kits : 3 rangées PORTRAIT · 10 PAYSAGE
rives 0,35 · allées 0,60 mini, dont 2,08 (cage)
et 1,39 – dégagt 0,30 (0,50 si cote douteuse)

sensibilités (même relevé, même moteur) :
100 % portrait / 100 % paysage → 160 / 152
dégagement 0,50 partout → 166
allées 1,00 (maintenance) → 164
allées 1,20 → 150


- caisson béton relevé — dégagt 0,30
- caisson à confirmer — dégagt 0,50
- local (cage, édicule) — murs épais
- cote mesurée (croquis Reda 27/07)
- cote / rattachement à confirmer

table PORTRAIT 1,134 × 4,70 (kit école)
2 modules 625 Wc, 15° — faîtage N-S
(module face OUEST | face EST)

table PAYSAGE 2,382 × 2,25
2 modules 625 Wc, 15° — même faîtage
N-S — les 2 kits VALIDÉS par le client 27/07

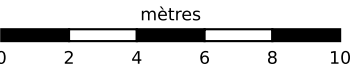

repérage croquis (IMG 2952-2955)

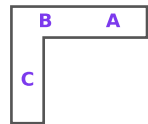

ACCORDIA TECH — Consultation FRDISI PV + stockage, Mohammedia

Bât. A (aile en L) — VUE DE TOITURE V2 : relevé + décisions client 27/07/2026 — 178 modules posables (111,2 kWc) — engagement 152 CONFIRMÉ +26

Relevé : R. Kasri — restitution TAQINOR — document de travail

A3 — cotes en m — échelle : barre graphique — NE REMPLACE PAS les planches 05E/05G