

VUE DE TOITURE DÉFINITIVE — BÂTIMENT B (AILE EN ARC) — RÉSIDENCE UNIVERSITAIRE UIB, MOHAMMEDIA — ASSEMBLAGE CORRIGÉ (client, 27/07/2026)

Arc en VRAIE géométrie (R_ext ≈ 274 m) — 3 SEGMENTS de toiture séparés par des MURETS HACHURÉS AU RAS (joints, ép. 0,45, h = 0 — confirmé client) : S1 20,55 (chaîne recalée) + joint + S2 ≈ 23,0 + joint + S3 ≈ 23,6 ≈ 68,1 m — TOUT RELEVÉ 27/07/2026, aucune zone « au plan »
cotes en mètres · bleu = mesuré/confirmé · orange = à confirmer · gris = déduit — calepinage : tables E-O 2,382 × 2,25 posées en tronçons droits par trame, PAR SEGMENT (les rangées s'arrêtent aux joints)


CALEPINAGE tables Est-Ouest 2,382 × 2,25 m (2 modules 625 Wc paysage) — 3 rangées suivant la courbe, PAR SEGMENT (tronçons droits par trame, arrêt aux joints)
allées 1,20 · rives 0,35 · rives d'extrémité 0,50 PAR SEGMENT · dégagement obstacles 0,30 (2 sens) — capacité géométrique ≈ 112 modules (S1 42 + S2 32 + S3 38) — INFORMATION d'étude, pas une promesse

ENGAGEMENT OFFRE : 120 modules — TENDU : posable relevé 112 (développé relevé ≈ 68 m vs ≈ 90 m aux plans — chaînes possiblement partielles, réconciliation site requise)

⚠ nota : capacité relevée ≈ 112 modules < 144 — la redistribution B → 144 (9×16) N'EST PAS absorbée par la géométrie relevée : à REVOIR (déport vers aile L à augmenter) — onduleurs/ratio à recalculer

DÉVELOPPÉ RELEVÉ ≈ 68 m (après retrait du doublon 3,82) — le « ≈ 90 × 11,2 » du dossier (§2.2, approximatif) reste À RÉCONCILIER — rien de masqué

joints : 2 murets hachurés AU RAS (h = 0), ép. 0,45 — CONFIRMÉ client — pas de rail à cheval sur un joint (dégagement 0,30 de part et d'autre)

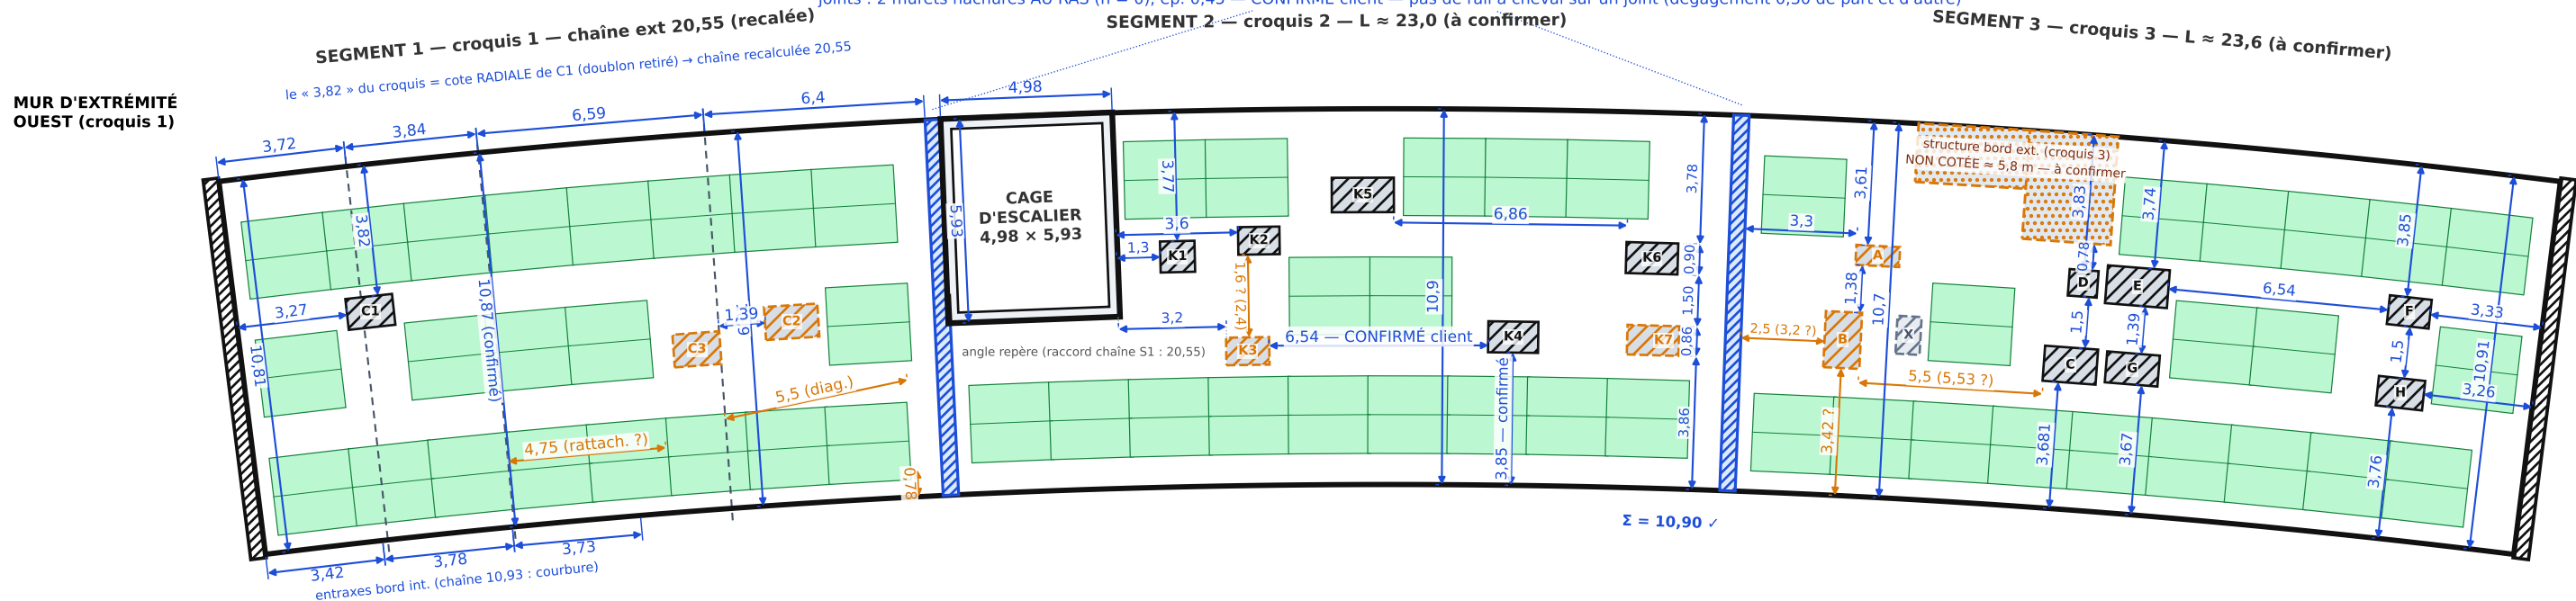

- table PV E-O (2 modules, 2,382 × 2,25)
- caisson béton relevé (chaîné)
- caisson — lecture / position à confirmer
- cage d'escalier (murs épais)
- muret AU RAS (h = 0, ép. 0,45) — joint, confirmé
- structure / caisson déduit du croquis (non coté)
- cote mesurée / confirmée (croquis Reda 27/07)
- cote / élément à confirmer



CONTRÔLES DE FERMETURE (relevé 27/07/2026) :

- S1 RECALCULÉE (vigilance client confirmée au zoom) : le « 3,82 » du croquis est la cote RADIALE bord ext → C1, PAS un entraxe — chaîne ext 3,72+3,84+6,59+6,4 = 20,55 ≡ joint S1/S2 + angle repère de la cage (raccord recalé)
- courbure : entraxes ext 11,38 vs int 10,93 → R_ext ≈ 274 m ; 10,93 ≡ 11,38 × R_int/R_ext ✓ — l'arc est DESSINÉ à cette géométrie
- S2 transversal K6/K7 : 3,78 + 0,90 + 1,50 + 0,86 + 3,86 = 10,90 ≡ largeur mesurée ✓ · K3→K4 = 6,54 CONFIRMÉ client (K4 s2 15,97-17,42 : aucun recouvrement K7 s2 20,10-21,60 ✓) · K4 → bord int = 3,85 CONFIRMÉ
- S3 radiales : 3,61+0,58+1,38+1,63+3,42 = 10,62 ≈ 10,7 (Δ 8 cm) ✓ · 3,681+1,02+1,50+0,77+3,83 = 10,80 ✓ · 3,74+1,10+1,39+0,90+3,67 = 10,80 ✓ · 3,85+0,84+1,50+0,86+3,76 = 10,81 ≈ 10,91 ✓
- développé : 20,55 + 0,45 + 23,0 + 0,45 + 23,6 = 68,05 ≈ 68 m (≈ 71,9 si le 3,82 était maintenu en entraxe — retiré au zoom) — écart vs dossier ≈ 90 AFFICHÉ ci-dessus

CAISSONS S1/S2 : C1 1,36×0,90 CONFIRMÉ (3,27 du mur ouest · 3,82 du bord ext · largeur 10,81 au mur) · C2 1,55×0,96 ? · C3 1,36×0,95 ? · K1 ≈1,0×0,9 · K2 ≈1,2×0,8 · K3 ≈1,25×0,8 ? · K4 ≈1,45×0,9 (position confirmée) · K5 ≈1,8×1,0 · K6 ≈1,5×0,9 · K7 1,5×0,86 · cage 4,98×5,93

CAISSONS S3 : A 1,27×0,58 ? (client : 0,58×0,27 — 1,27 retenu, la chaîne radiale ferme) · B 1,05×1,63 ? (2° nombre lu 1,63/1,03) · X non coté (gris) · C 1,54×1,02 (1,64 ?) · D 0,84×0,77 · E 1,80×1,10 · G 1,53×0,9 · F 1,22×0,84 (0,86 lu) · H 1,35×0,86

S3 — À RÉCONCILIER : cote croquis « 6,59 » (C→G) INCOMPATIBLE avec l'ancrage droit (E = F = 6,54 ; F/H ancrés 3,33/3,26 du bord est) pour L ≈ 23,6 — position E/G retenue par l'ancrage DROIT + fermetures radiales ; orientation croquis 3 supposée = croquis 2 (bord haut = ext.)

POSE PV : rails en TRONÇONS DROITS par trame — reprise angulaire ≈ 0,5°/table (éclisses) ; rangées PAR SEGMENT, jamais à cheval sur un joint

À CONFIRMER (orange) : positions C2/C3 (recalées au joint) · K3 · 1,6/2,4 · rattachements 4,75/5,5/0,78/0,97×2 (S1) · lectures S3 : 2,5/3,2 · 5,5/5,53 · 3,42 · A · B · structure bord ext (≈ 5,8 m, paliers ≈ 1,7/3,15) · X · L S2 ≈ 23,0 · L S3 ≈ 23,6 · mur est

À CONFIRMER (suite) : les chaînes de chaque segment couvrent-elles bout en bout (muret à muret) ? question posée au client — si chaînes partielles, développé et posable remontent

RÉSERVE DRV (mémoire) : NON vue au relevé — position à fixer en étude d'exécution (dégagement ≥ 1 m)

ACCORDIA TECH — Consultation FRDISI PV + stockage, Mohammedia

Bât. B — AILE EN ARC — VUE EN ARC (R_ext ≈ 274 m) — ASSEMBLAGE CORRIGÉ 3 SEGMENTS — DÉFINITIVE

Relevé : R. Kasri 27/07/2026 (TOUT relevé) — restitution TAQINOR

Échelle ≈ 1:200 (A3) — cotes en mètres — NE REMPLACE PAS 05E/06G