

VUE DE TOITURE — BÂTIMENT C (ÉCOLE SUPTECH, MOHAMMEDIA) — 26,2 × 51,1 m (plan)


Relevé terrain 27/07/2026 — croquis = TOIT COMPLET 51,1 m (bord bas = mur sud) — bleu = mesuré · orange = à confirmer · gris = déduit — cage 4,11×≈14,42 (prof. DÉDUITE) + local 4,18×4,50 — gène 4,78×≈3,2? (muret h≈0,5, nature ?) à 13,5 du mur sud — tables E-O PORTRAIT 1,134×4,70 (pose 15°), retenu 1,20/0,35/0,30 (gène 0,50)

ENGAGEMENT 288 : TENDU — 264 modules posables sur 51,1 m (manque 24) — voir redistribution

total toit complet 51,1 m (planches 1,20 / 0,35 / 0,30 (gène 0,50)) : 264 mod. = 165,00 kWc — conservateur 1,50/0,50/0,50 : 260 — marge vs 288 : -24

cage · profondeur ≈14,42 DÉDUITE de la fermeture 51,1 (jamais cotée au croquis) — à confirmer sur site (question posée au client)

Δ 0,58 (plan — mesuré) à confirmer

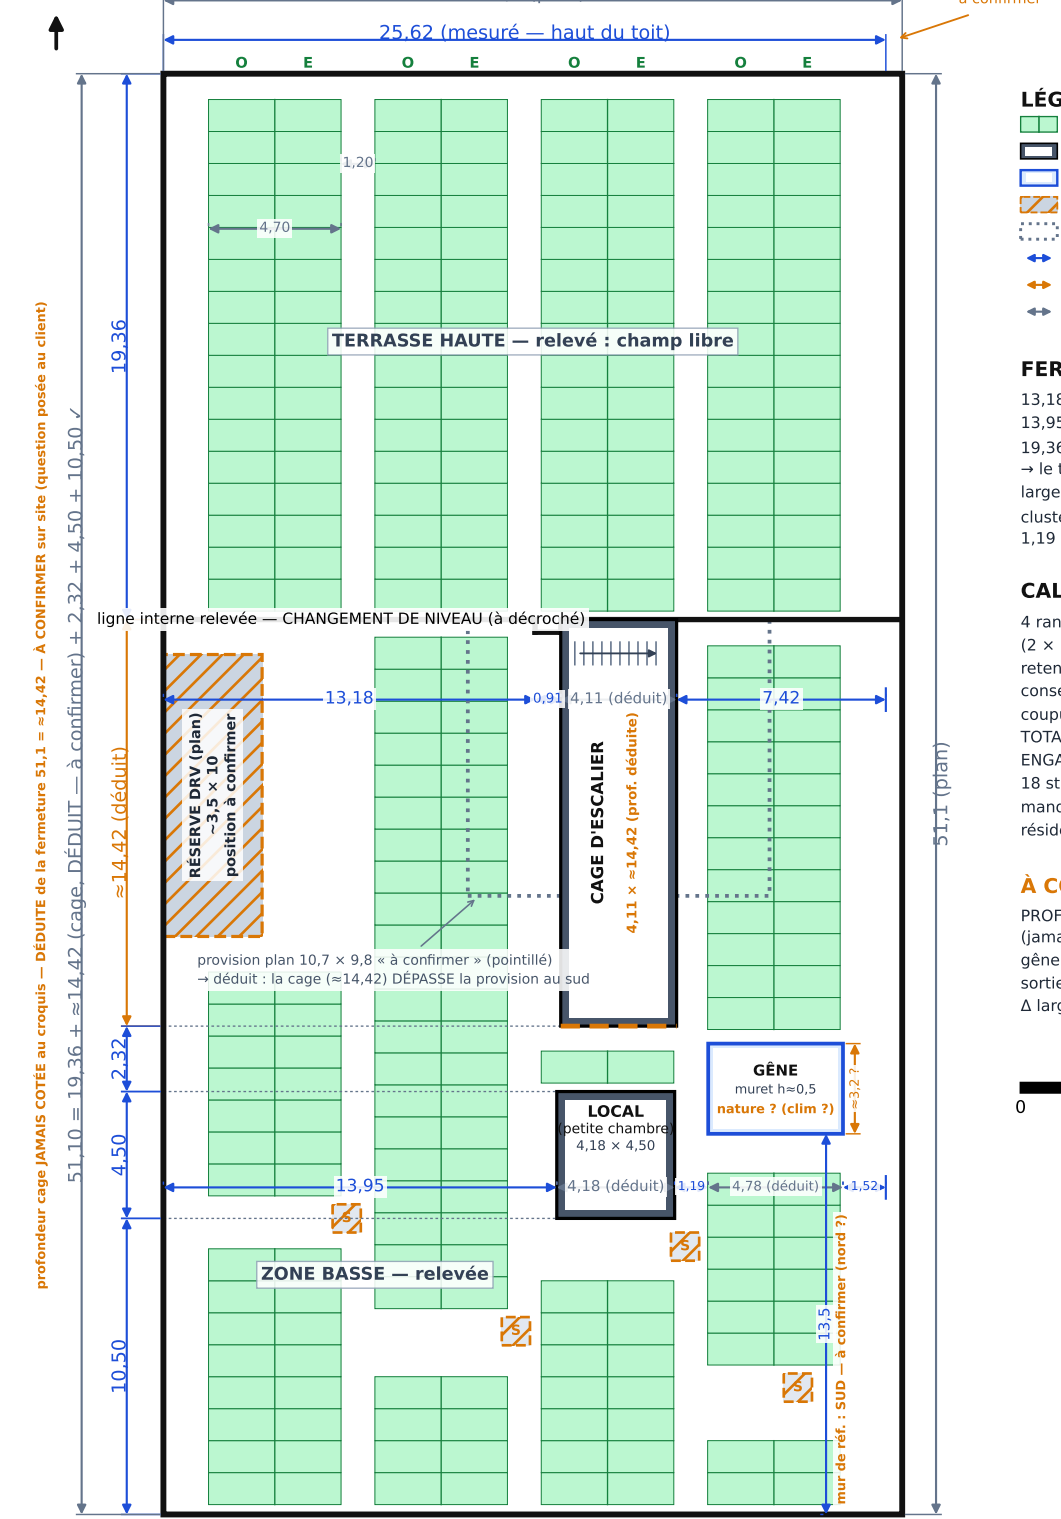

LÉGENDE

- table E-O portrait 1,134×4,70 — 2 modules 625 Wc, pose 15°
- volume relevé (cage 4,11×≈14,42 déduit · local 4,18×4,50)
- gène 4,78×≈3,2? — muret h≈0,5 (nature ? · dégagt 0,50)
- réserve / obstacle bloqué (S = souche · dégagt 0,30)
- provision plan (pointillé — dépassée au sud par la cage)
- cote MESURÉE / confirmée site (bleu)
- cote / position À CONFIRMER
- plan / déduit des fermetures

FERMETURES DU CROQUIS (corrigées)


13,18 + 0,91 (marche) + 4,11 (déduit) + 7,42 = 25,62 ✓ exact
13,95 + 4,18 (déduit) + 1,19 + 4,78 (déduit) + 1,52 = 25,62 ✓
19,36 + ≈14,42 (cage, DÉDUIT) + 2,32 + 4,50 + 10,50 = 51,10 ✓
→ le tronçon jamais coté du croquis = la PROFONDEUR DE LA CAGE
largeur : 25,62 mesuré vs 26,2 plan → Δ 0,58 à confirmer
cluster SE : le petit rectangle = LA GÈNE (4,78 × ≈3,2 ?) · 1,19 = écart chambre↔gène · 13,5 = gène → mur sud (position)

CALEPINAGE — PORTRAIT 15°

4 rangées de tables E-O PORTRAIT 1,134 × 4,70
(2 × 2,382 × cos15° + faîtage) le long des 51,1 m
retenu : allées 1,20 · rives 0,35 · dégagt 0,30 (gène : 0,50)
conservateur 1,50/0,50/0,50 : 260 mod. (information)
coupure de niveau à la ligne interne (aucun chevauchement)
TOTAL toit complet 51,1 m : 264 mod. = 165,00 kWc
ENGAGEMENT : 288 modules (18×16) = 180,0 kWc → TENDU
18 strings × 16 — 3 onduleurs 50 kW (96/96/96)
manque 24 modules → déport possible vers la résidence · redistribution inter-bâtiments (ratios [0,75;1])

À CONFIRMER (orange)

PROFONDEUR CAGE ≈14,42 : DÉDUITE de la fermeture 51,1 (jamais cotée au croquis) — question posée au client
gène : prof. ≈3,2 ? · muret h≈0,5 · nature ? (probable sortie clim) · mur de réf. du 13,5 : SUD retenu (nord ?)
Δ largeur 0,58 · positions : DRV ouest ~3,5×10 · 4 souches ~1×1

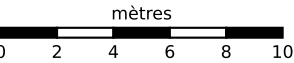

Croquis client = toit COMPLET (bord bas = mur sud) : un seul calepinage sur 51,1 m. Aucune table à cheval sur la ligne interne.

GÈNE : ouvrage 4,78 × ≈3,2 ? (muret h≈0,5), nature à préciser (probable sortie clim) — bord sud à 13,5 du MUR SUD (réf. à confirmer — nord ?) — bloquée, dégagt 0,50

NOTA : déport possible vers la résidence à l'exécution (inverse de la redistribution résidence).

Arbitrage possible par redistribution inter-bâtiments (ratios par installation restent dans [0,75 ; 1]) — voir note de synthèse.

ACCORDIA TECH — Consultation FRDISI PV + stockage, Mohammedia

BÂT. C — ÉCOLE SUPTECH — VUE DE TOITURE (relevé + calepinage)

Relevé R. Kasri 27/07/2026 — restitution TAQINOR — tables E-O portrait 1,134×4,70, pose 15°

Échelle : barre graphique (impression A3) — cotes en mètres — NE REMPLACE PAS 05E/05G