

VUE DE TOITURE — BÂTIMENT C (ÉCOLE SUPTECH, MOHAMMEDIA) — 26,2 × 51,1 m (plan)


Relevé terrain 27/07/2026 — croquis = TOIT COMPLET 51,1 m — bleu = mesuré · orange = à confirmer · gris = déduit — cage 4,11×≈8,82 (client ≈8,5) · local 4,18×4,50 à 7,92 · gêne 4,78×≈1,0 — souches/clim : NÉANT (client 27/07) — tables E-O portrait 1,134×4,70 (15°), allées 0,60 optimisées

ENGAGEMENT 288 (18×16) : CONFIRMÉ — 314 modules posables sur le relevé complet 51,1 m

total toit complet 51,1 m (allées 0,60 optimisées / rives 0,35 / dégagt 0,30 (gêne 0,50)) : 314 mod. = 196,25 kWc — conservateur 1,50/0,50/0,50 : 314 — marge vs 288 : +26

cage : segment cage→local RELEVÉ 7,92 (réponse client 27/07) → profondeur ≈8,82 déduite de la fermeture 51,1 (client : ≈8,5 arrondi) — à confirmer à l'exécution

Δ 0,58 (plan — mesuré)
à confirmer

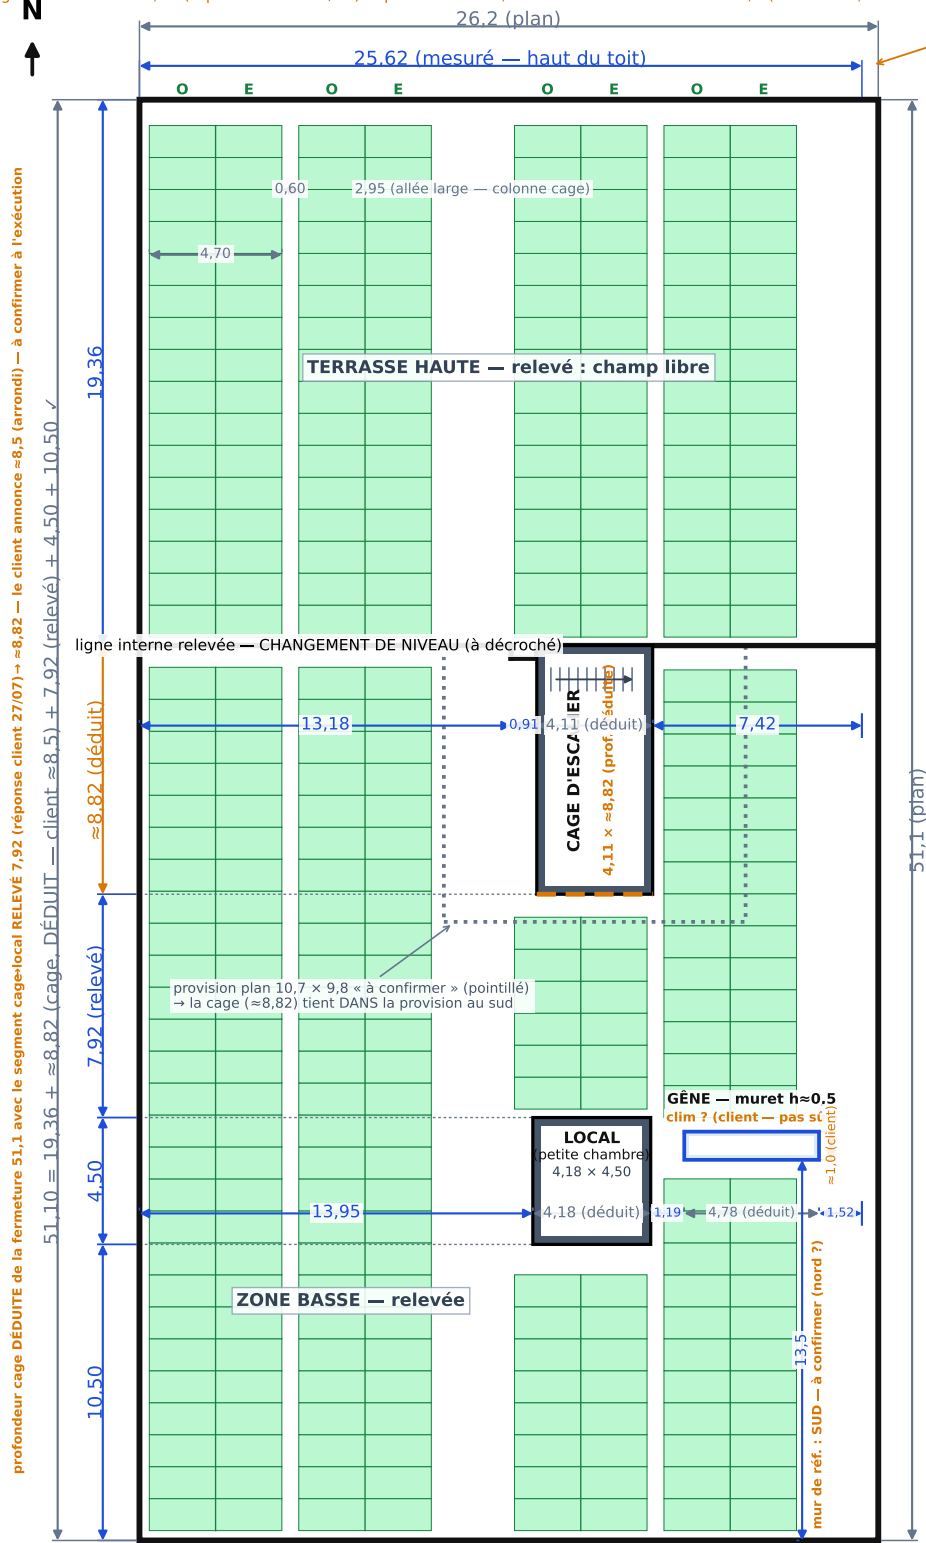

LÉGENDE

- table E-O portrait 1,134×4,70 — 2 modules 625 Wc, pose 15°
- volume relevé (cage 4,11×≈8,82 déduit · local 4,18×4,50)
- gêne 4,78×≈1,0 (client) — muret h≈0,5, clim ? · dégagt 0,50
- provision plan (pointillé — la cage ≈8,82 tient dedans)
- cote MESURÉE / confirmée site (bleu)
- cote / position À CONFIRMER
- plan / déduit des fermetures

FERMETURES DU CROQUIS (corrigées)


13,18 + 0,91 (marche) + 4,11 (déduit) + 7,42 = 25,62 ✓ exact
13,95 + 4,18 (déduit) + 1,19 + 4,78 (déduit) + 1,52 = 25,62 ✓
19,36 + ≈8,82 (cage, DÉDUIT) + 7,92 (relevé) + 4,50 + 10,50 = 51,10 ✓
→ cage→local = 7,92 RELEVÉ (réponse client 27/07, remplace 2,32) ;
le tronçon déduit reste la PROFONDEUR DE LA CAGE (client ≈8,5)
largeur : 25,62 mesuré vs 26,2 plan → Δ 0,58 à confirmer
cluster SE : le petit rectangle = LA GÊNE (4,78 × ≈1,0 client) ·
1,19 = écart chambre→gêne · 13,5 = gêne → mur sud (position)

CALEPINAGE — PORTRAIT 15°

4 rangées de tables E-O PORTRAIT 1,134 × 4,70
(2 × 2,382 × cos15° + faitage) le long des 51,1 m
retenu : allées 0,60 OPTIMISÉES (client 27/07) — surplus
concentré en UNE allée large 2,95 sur la colonne cage/local
→ cage+local+marche ne coupent qu'1 bande ; gêne : 1 bande
rives 0,35 · dégagt 0,30 (gêne : 0,50)
info : uniforme 0,60 = 314 · conservateur 1,50/0,50 = 314
coupure de niveau à la ligne interne (aucun chevauchement)
TOTAL toit complet 51,1 m : 314 mod. = 196,25 kWc
ENGAGEMENT : 288 modules (18×16) = 180,0 kWc → CONFIRMÉ
18 strings × 16 — 3 onduleurs 50 kW (96/96/96)
marge : +26 modules (cage prof. déduite ≈8,82)

À CONFIRMER (orange)

PROFONDEUR CAGE ≈8,82 : DÉDUITE de la fermeture 51,1 avec
le segment 7,92 relevé (réponse client 27/07 ; il annonce ≈8,5
arrondi) — à confirmer à l'exécution
gêne : ≈1,0 prof (client) · muret h≈0,5 · clim ? (pas sûr)
— dégagt 0,50 maintenu · mur de réf. du 13,5 : SUD (nord ?)
Δ largeur 0,58 · CLIM FUTURE : aucune aujourd'hui, viendra
après → implantation à coordonner avec le champ PV (exécution)

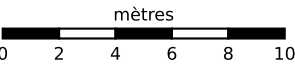

Croquis client = toit COMPLET (bord bas = mur sud) : un seul calepinage sur 51,1 m. Aucune table à cheval sur la ligne interne.
GÊNE : 4,78 × ≈1,0 (client — muret h≈0,5, clim ? pas sûr) — dégagt 0,50 · SOUCHES : aucune vue (client 27/07).
CLIM : aucune aujourd'hui — viendra plus tard (client 27/07) → à coordonner avec le champ PV à l'exécution.

ACCORDIA TECH — Consultation FRDISI PV + stockage, Mohammedia

BÂT. C — ÉCOLE SUPTECH — VUE DE TOITURE (relevé + calepinage)

Relevé R. Kasri 27/07/2026 — restitution TAQINOR — tables E-O portrait 1,134×4,70, pose 15°

Échelle : barre graphique (impression A3) — cotes en mètres — NE REMPLACE PAS 05E/05G