


RELEVÉ CONTRADICTOIRE TOITURE — BÂTIMENT A (AILE EN L) — RÉSIDENCE UNIVERSITAIRE UIB

Géométrie d'ensemble : plans reçus (mémoire §2.1 — aile 1 ≈ 48×11 m, aile 2 ≈ 40,5×11,2 m) · cotes RELEVÉES le 27/07/2026 (croquis A/B/C) — GRIS = plan · BLEU = mesuré · ORANGE = à confirmer

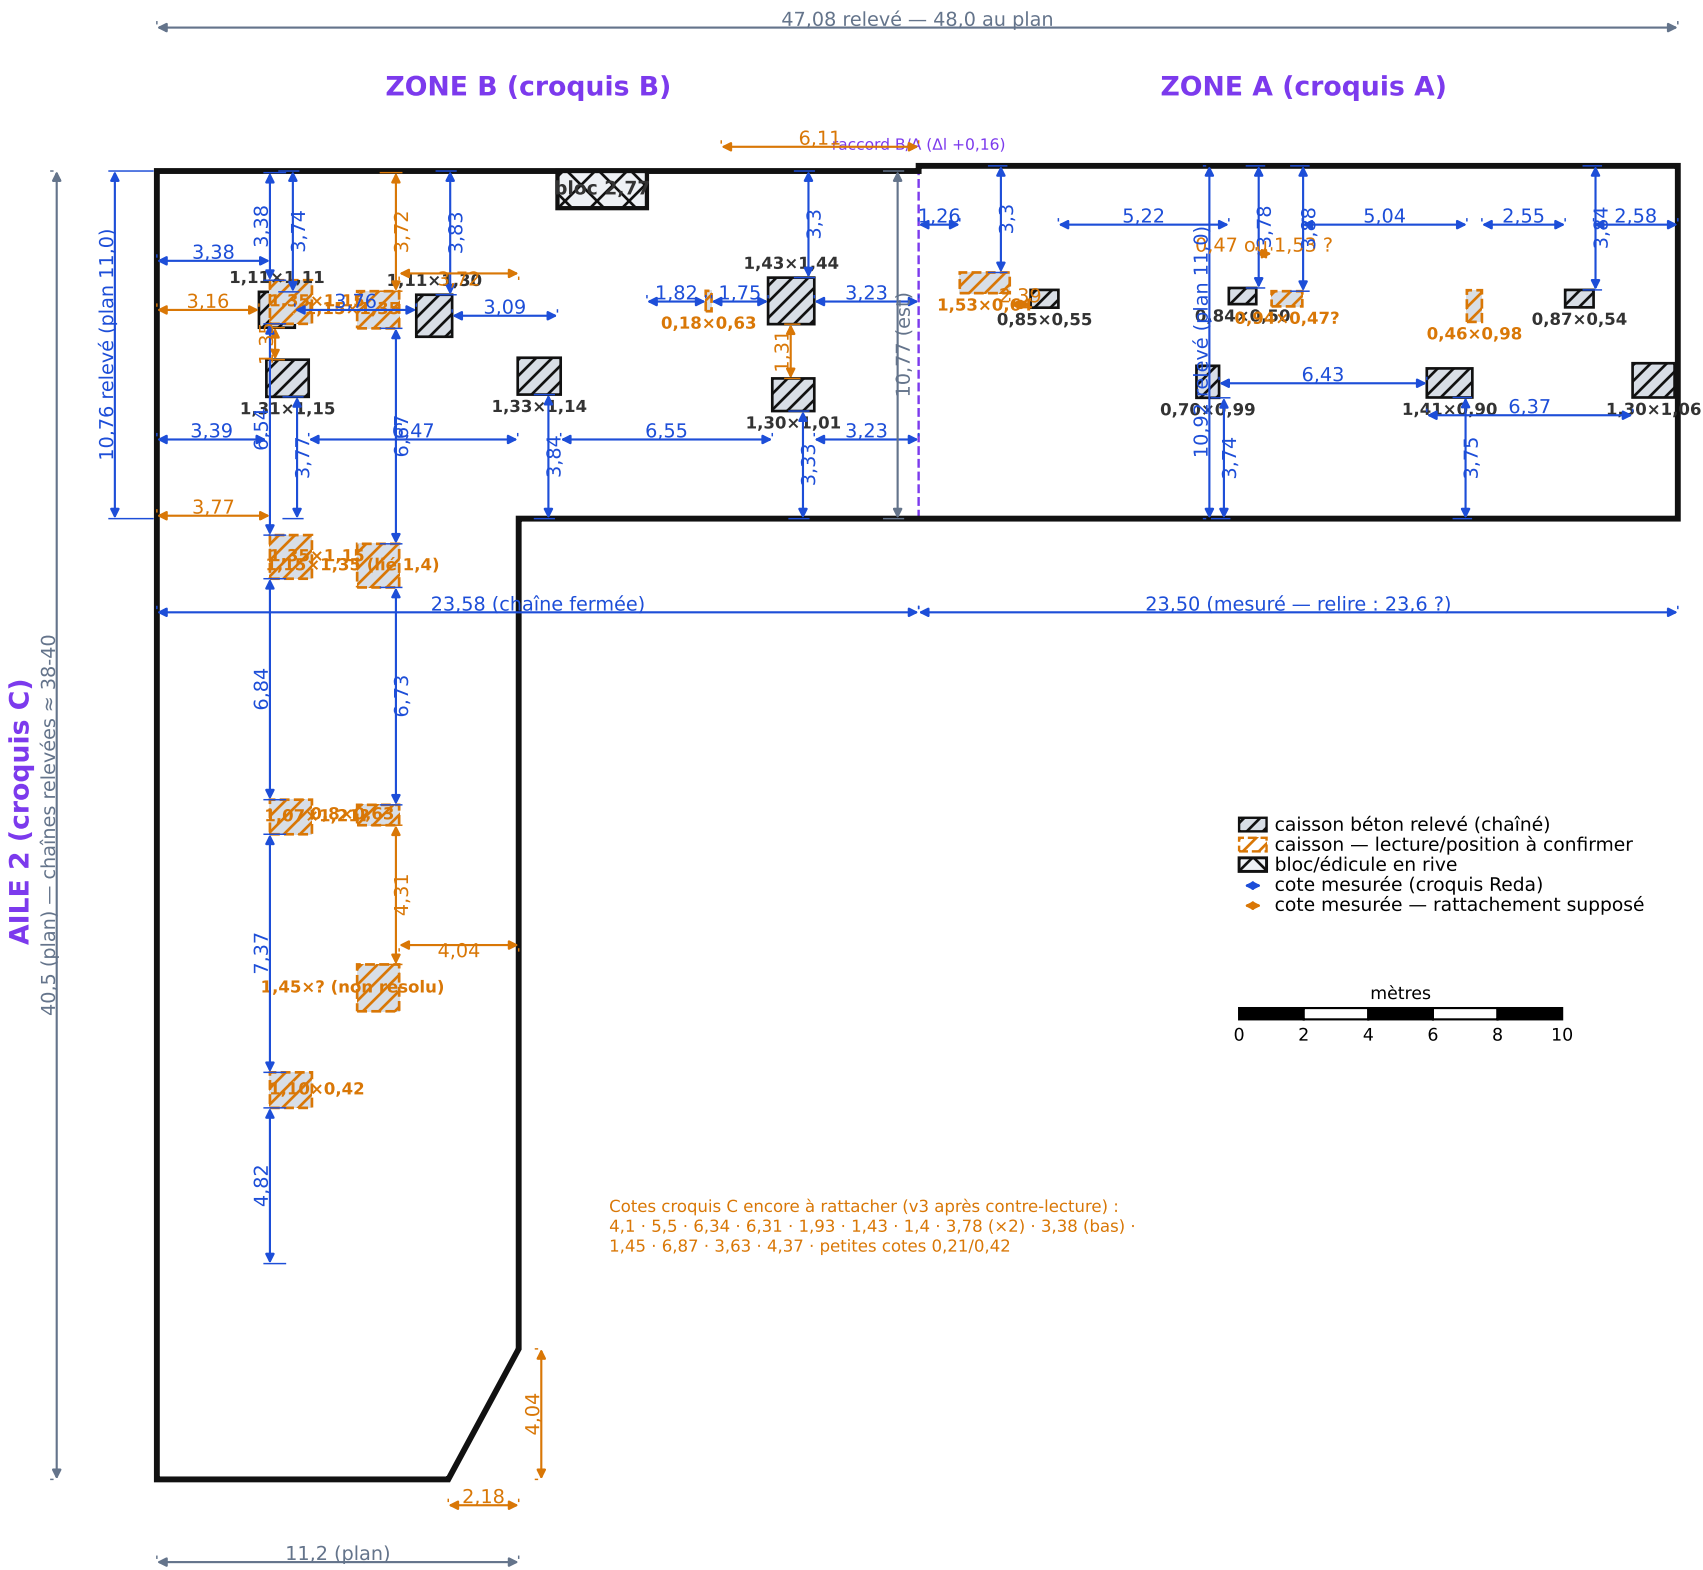

ACCORDIA TECH — Consultation FRDISI PV + stockage, Mohammedia

Bât. A — aile en L (48×11 + 40,5×11,2 au plan) — RELEVÉ RECONSTITUÉ v2

Relevé : R. Kasri, 27/07/2026 — restitution TAQINOR (document de travail)

Échelle ~1:250 (A3) — cotes en m — NE REMPLACE PAS les planches 05E/05G