


RELEVÉ CONTRADICTOIRE TOITURE — BÂTIMENT C (ÉCOLE SUPTECH)

Reconstruction cotée du croquis terrain du 27/07/2026 — cotes en mètres · bleu = mesuré · orange = lecture/rattachement à confirmer · gris = déduit des fermetures

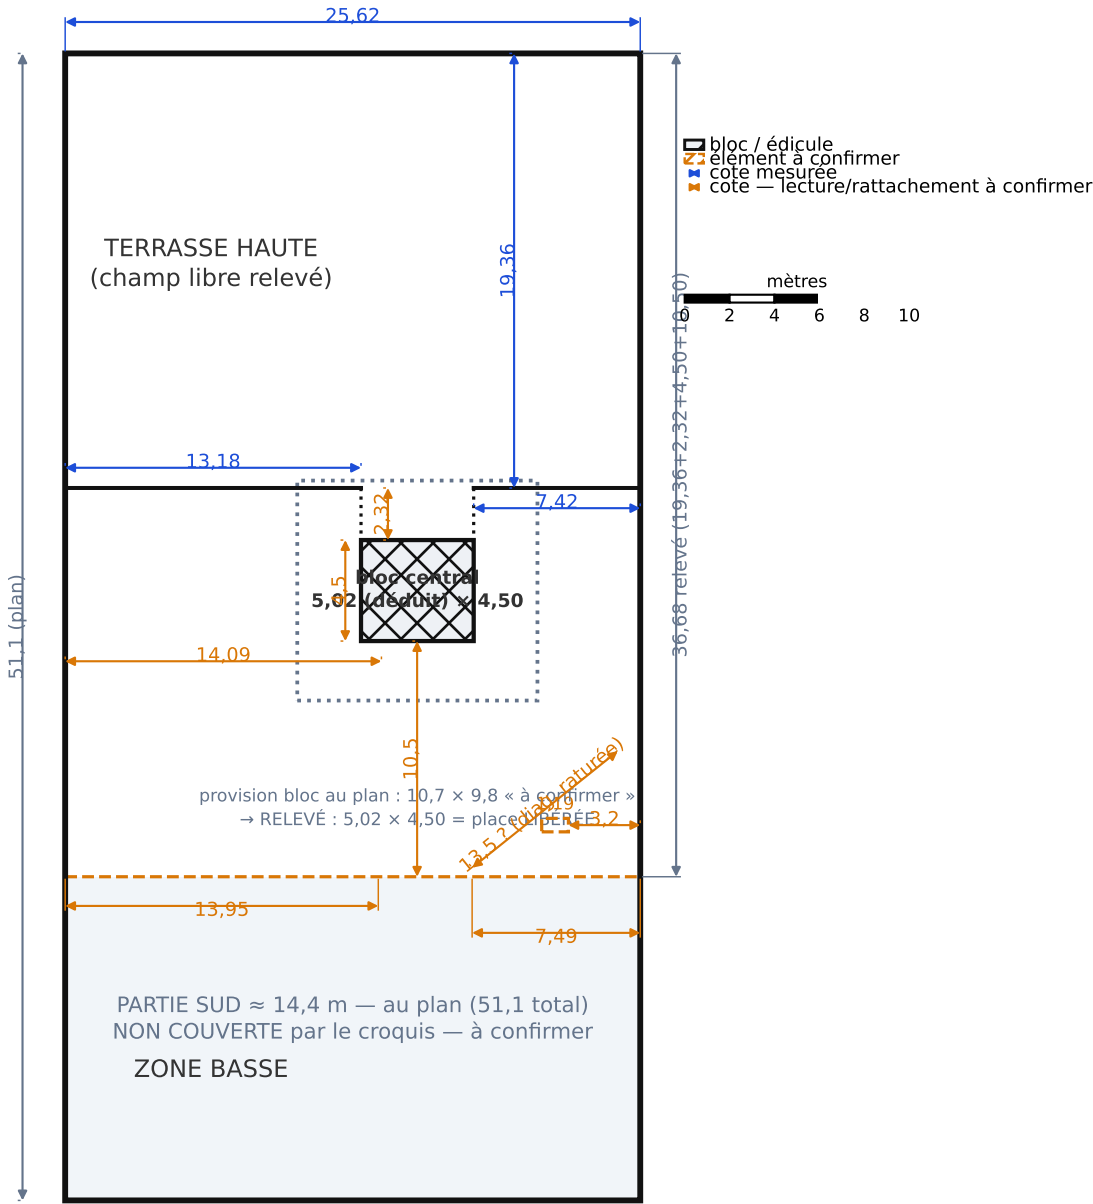

FERMETURES : 13,18 + 5,02 + 7,42 = 25,62 ✓ exact (largeur bloc déduite) · profondeur totale 36,68 déduite de 19,36+2,32+4,50+10,50
À CONFIRMER (lecture croquis) : 2,32 · 4,5 (ou 5,4 ?) · 10,5 (ou 1,05 ?) · 14,09 (rattachement) · 13,95 (extrémité) · cluster SE (1,19 / 3,2 / 7,49 / 13,5 raturé / 1,52 ?)

ACCORDIA TECH — Consultation FRDISI PV + stockage, Mohammedia

Bât. C — ÉCOLE SUPTECH (26,2 x 51,1 au plan) — RELEVÉ RECONSTITUÉ v2

Relevé : R. Kasri, 27/07/2026 — restitution TAQINOR (document de travail)

Échelle 1:250 (A3) — cotes en mètres — NE REMPLACE PAS les planches 05E/05G