


CALEPINAGE SUR RELEVÉ (moteur corrigé) — BÂT. A (AILE EN L) — tables E-O paysage

Dégagement obstacles appliqué dans les 2 sens + rives d'extrémité 0,50 — allées 1,20 · rives 0,35 — LE RELEVÉ MONTRE QUE A SEUL NE PORTE PAS 152 : redistribution A 128 / B 144 (voir nota)

POSABLE HONNÊTE BÂT. A : 144 modules (90.0 kWc) — ligne bordereau A : 152

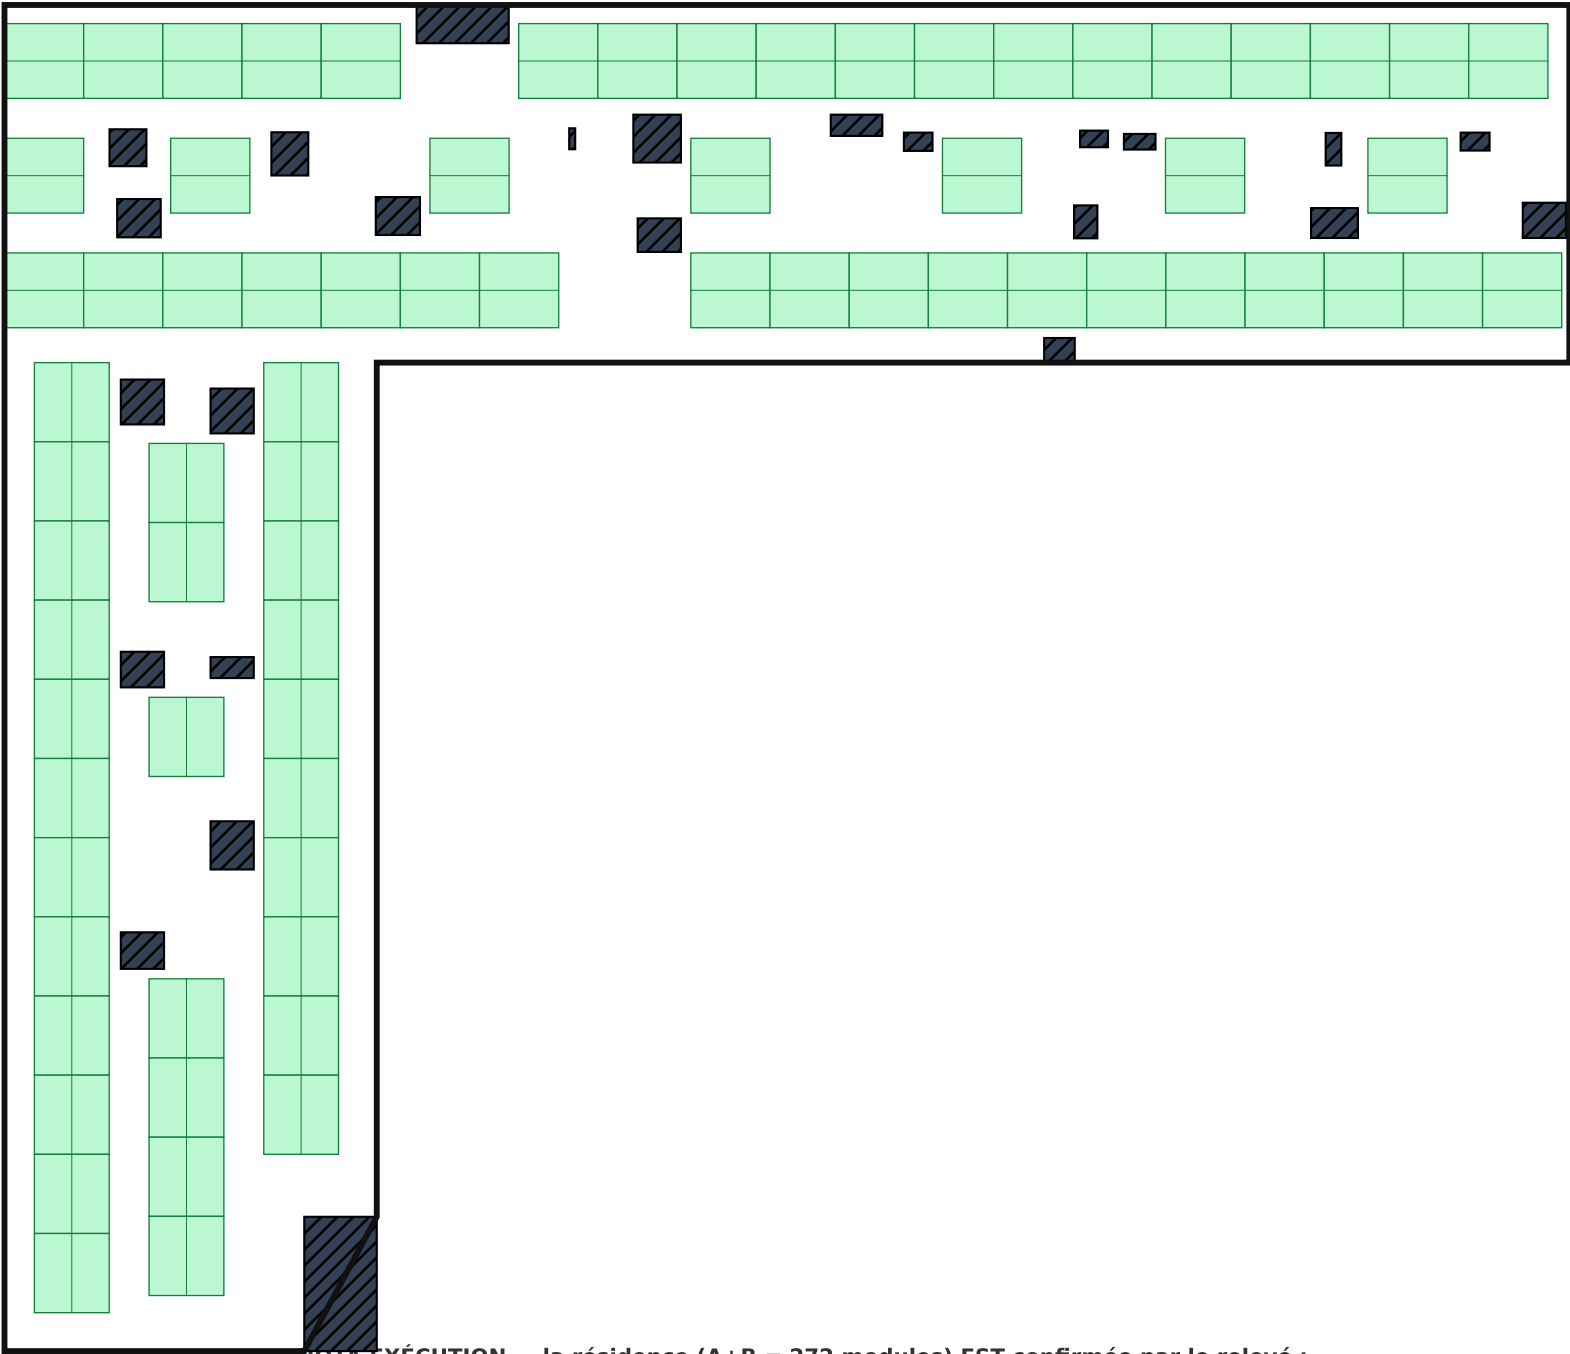

NOTA EXÉCUTION — la résidence (A+B = 272 modules) EST confirmée par le relevé : redistribution A = 128 (8×16) + B = 144 (9×16) -> 17 chaînes de 16, AUCUNE chaîne de 8, charges onduleurs 96/80/96 et ratio 150/170 = 0,882 INCHANGÉS — marché à prix unitaires, implantation ajustée au relevé contradictoire (mémoire §2.1).

ACCORDIA TECH — FRDISI PV, Mohammedia

Bât. A (L) — CALEPINAGE FINAL corrigé — posable 144 / redistribution 128

Relevé R. Kasri 27/07/2026 — restitution TAQINOR — document de travail

Tables E-O paysage 2,382×2,25 — audit adversarial appliqué — NE REMPLACE PAS 05G/06G