


VUE DE TOITURE — BÂTIMENT A (AILE EN L) — RÉSIDENCE UNIVERSITAIRE UIB, MOHAMMEDIA

Contour, locaux et obstacles : RELEVÉ CONTRADICTOIRE du 27/07/2026 (croquis A/B/C) — calepinage superposé : tables E-O 2,382×2,25 m, 3 rangées/bande, allées 1,20, rives 0,35, rives d'extrémité 0,50, dégagement obstacles 0,30 (2 sens), phase optimisée — BLEU = mesuré · ORANGE = à confirmer · GRIS = plan/déduit

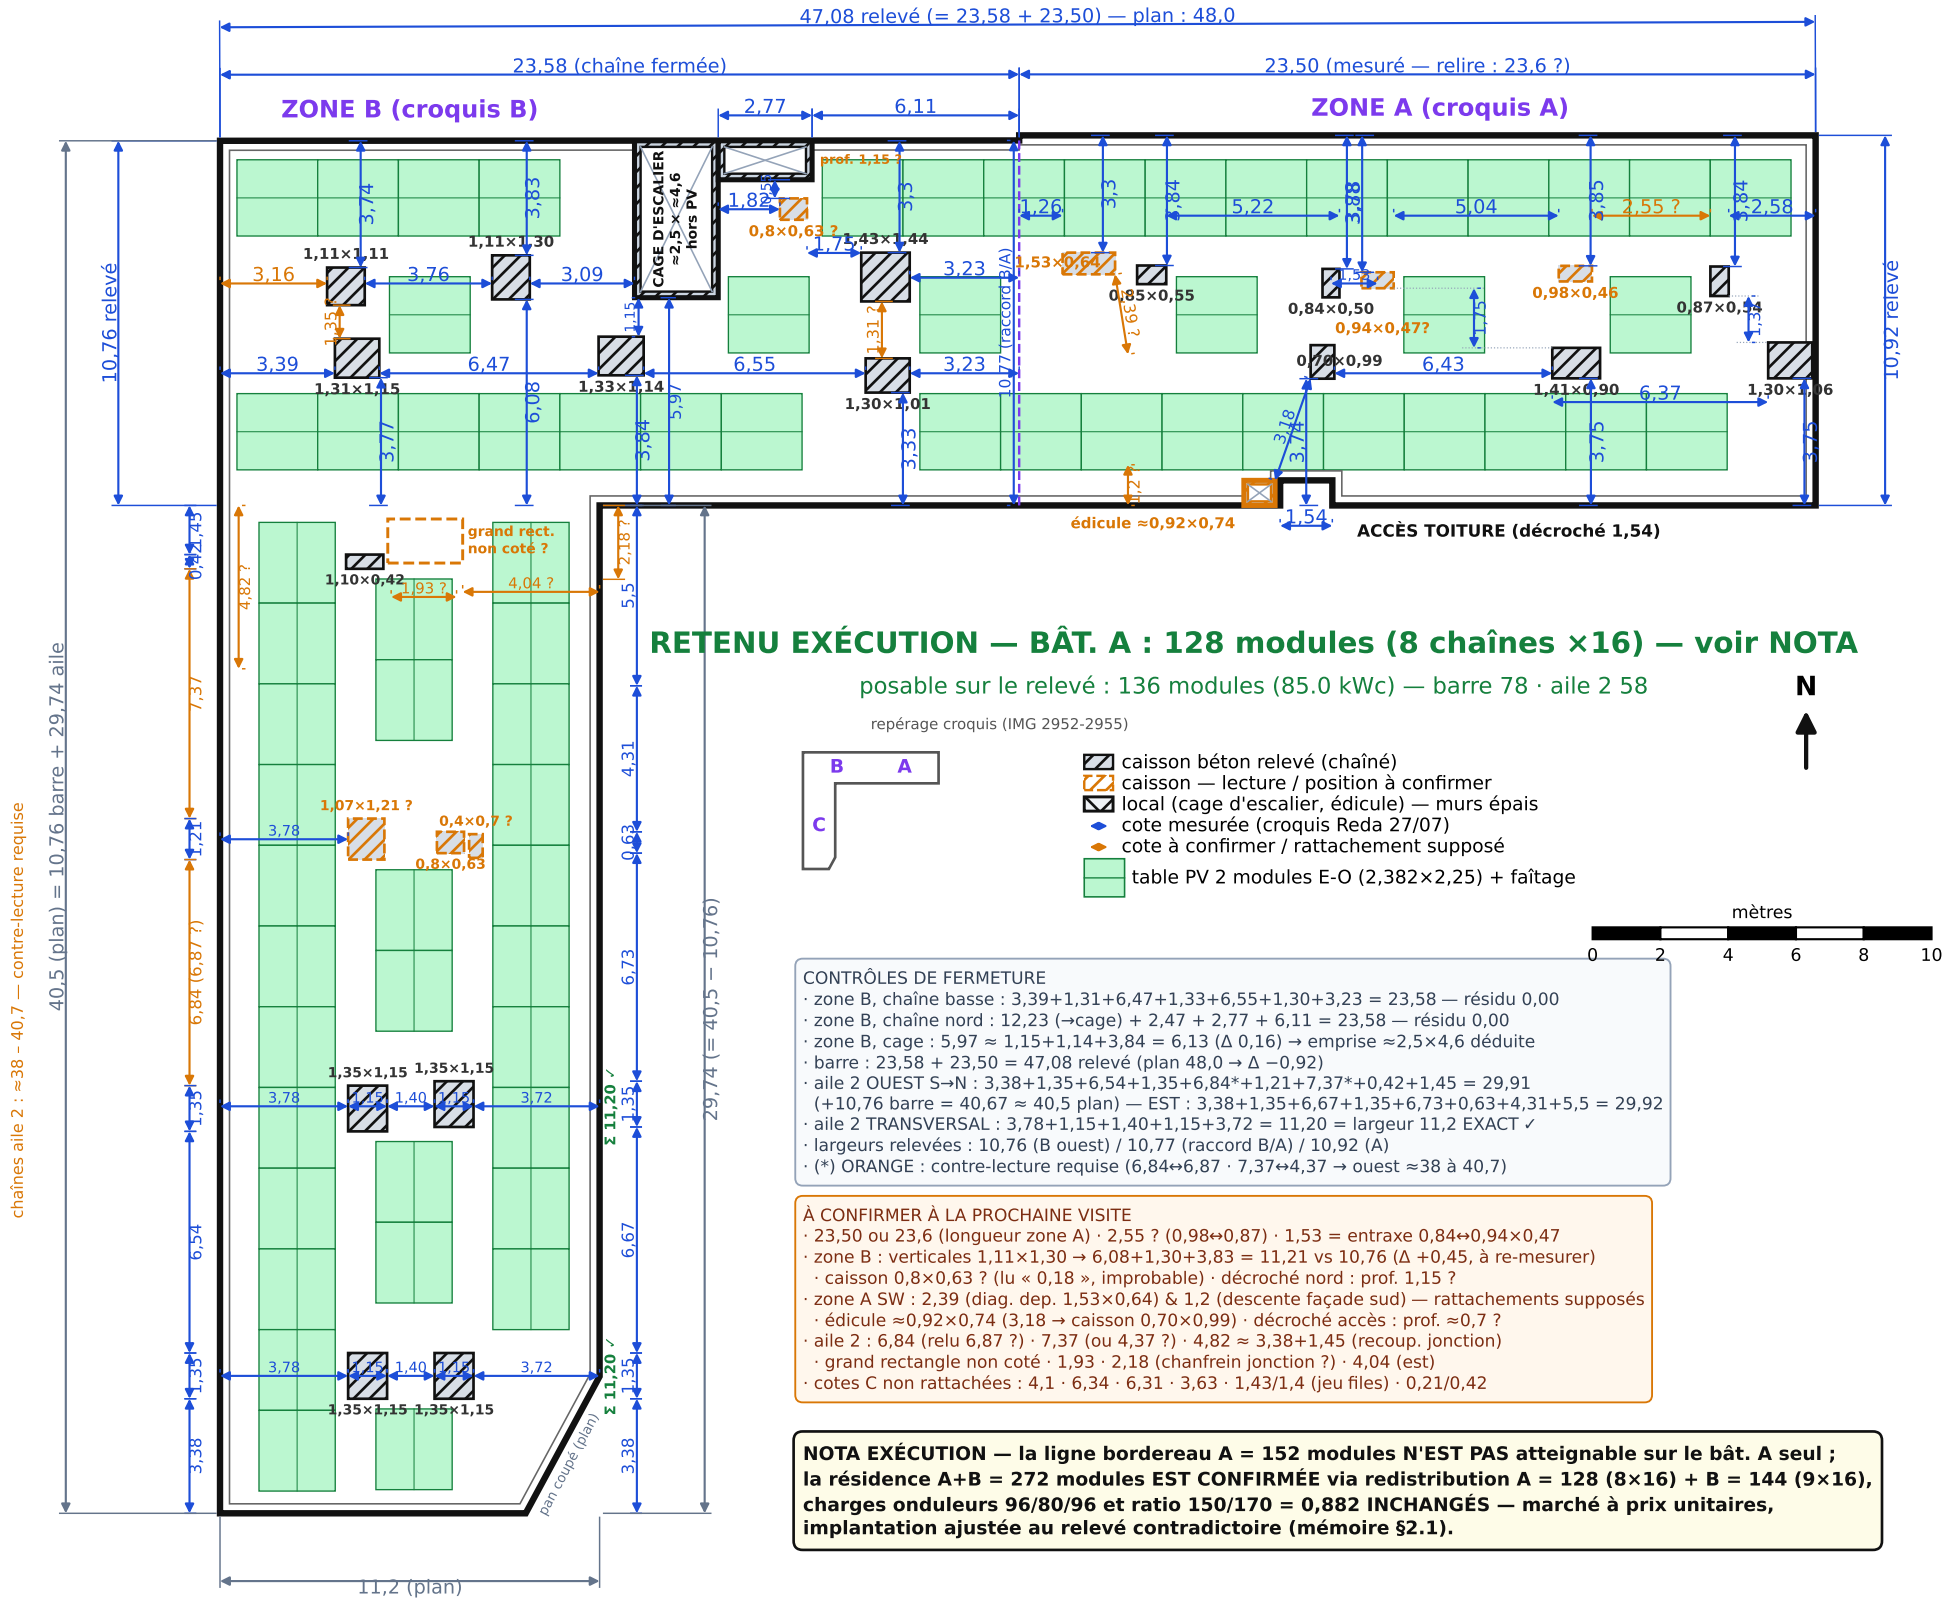

ACCORDIA TECH — Consultation FRDISI PV + stockage, Mohammedia

Bât. A (aile en L) — VUE DE TOITURE : relevé 27/07/2026 — exécution 128 mod. (posable 136)

Relevé : R. Kasri — restitution TAQINOR — document de travail

A3 — cotes en m — échelle : barre graphique — NE REMPLACE PAS les planches 05E/05G